



THIS TRIM SHOWN ON
SECTION A-A SHEET#5




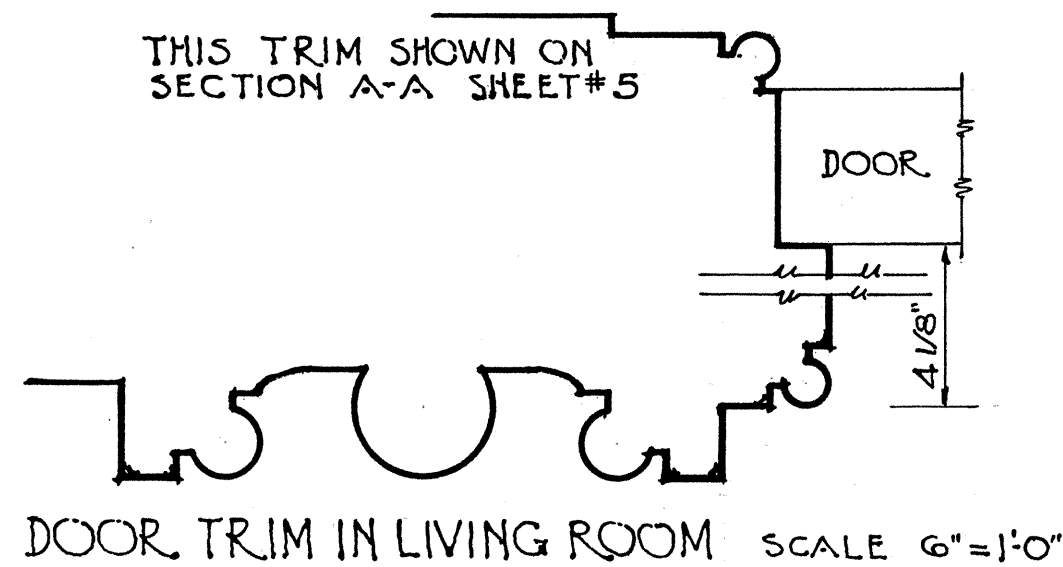


DOOR SCHEDULE

MARK	SIZE
A	3'-0" X 6'-4" X 1 5/8"
B	2'-8" X 6'-4" X 1 5/8"
C	2'-6" X 6'-4" X 1 5/8"
D	2'-0" X 5'-9" X 1 5/8"
E	3'-6" X 7'-1" X 1 3/4"
F	3'-0" X 7'-2" X 1 5/8"
G	2'-8" X 7'-2" X 1 5/8"
H	3'-2" X 6'-1" X 1 3/4"
I	2'-2" X 7'-2" X 1 5/8"
J	7'-5" X 8'-4" X 1 5/8"
K	4'-2" X 7'-2" X 1 5/8"
L	3'-0" X 7'-0" X 1 5/8"
M	2'-0" X 6'-6" X 1 3/4"

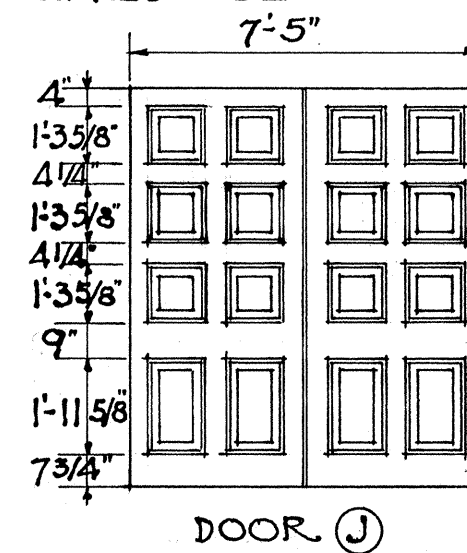

PROFILE OF DOOR PANELS SCALE FULL SIZE

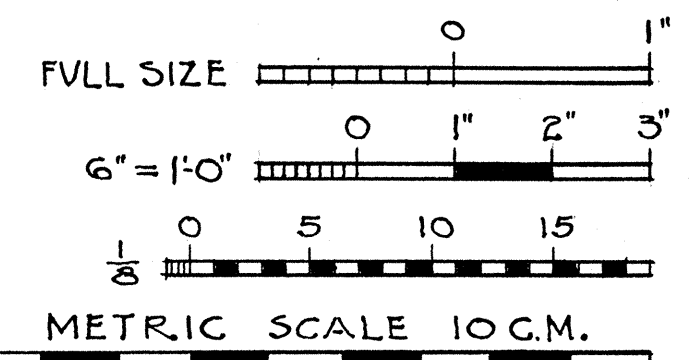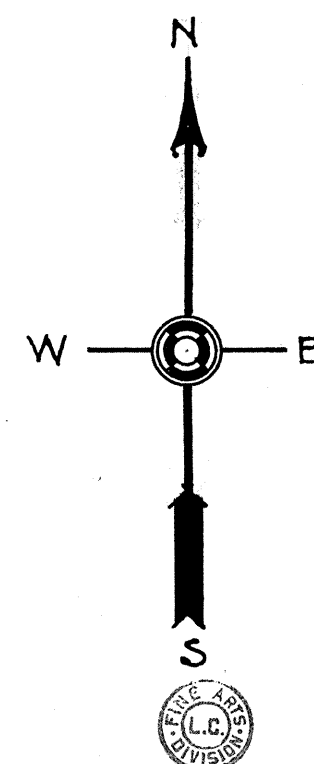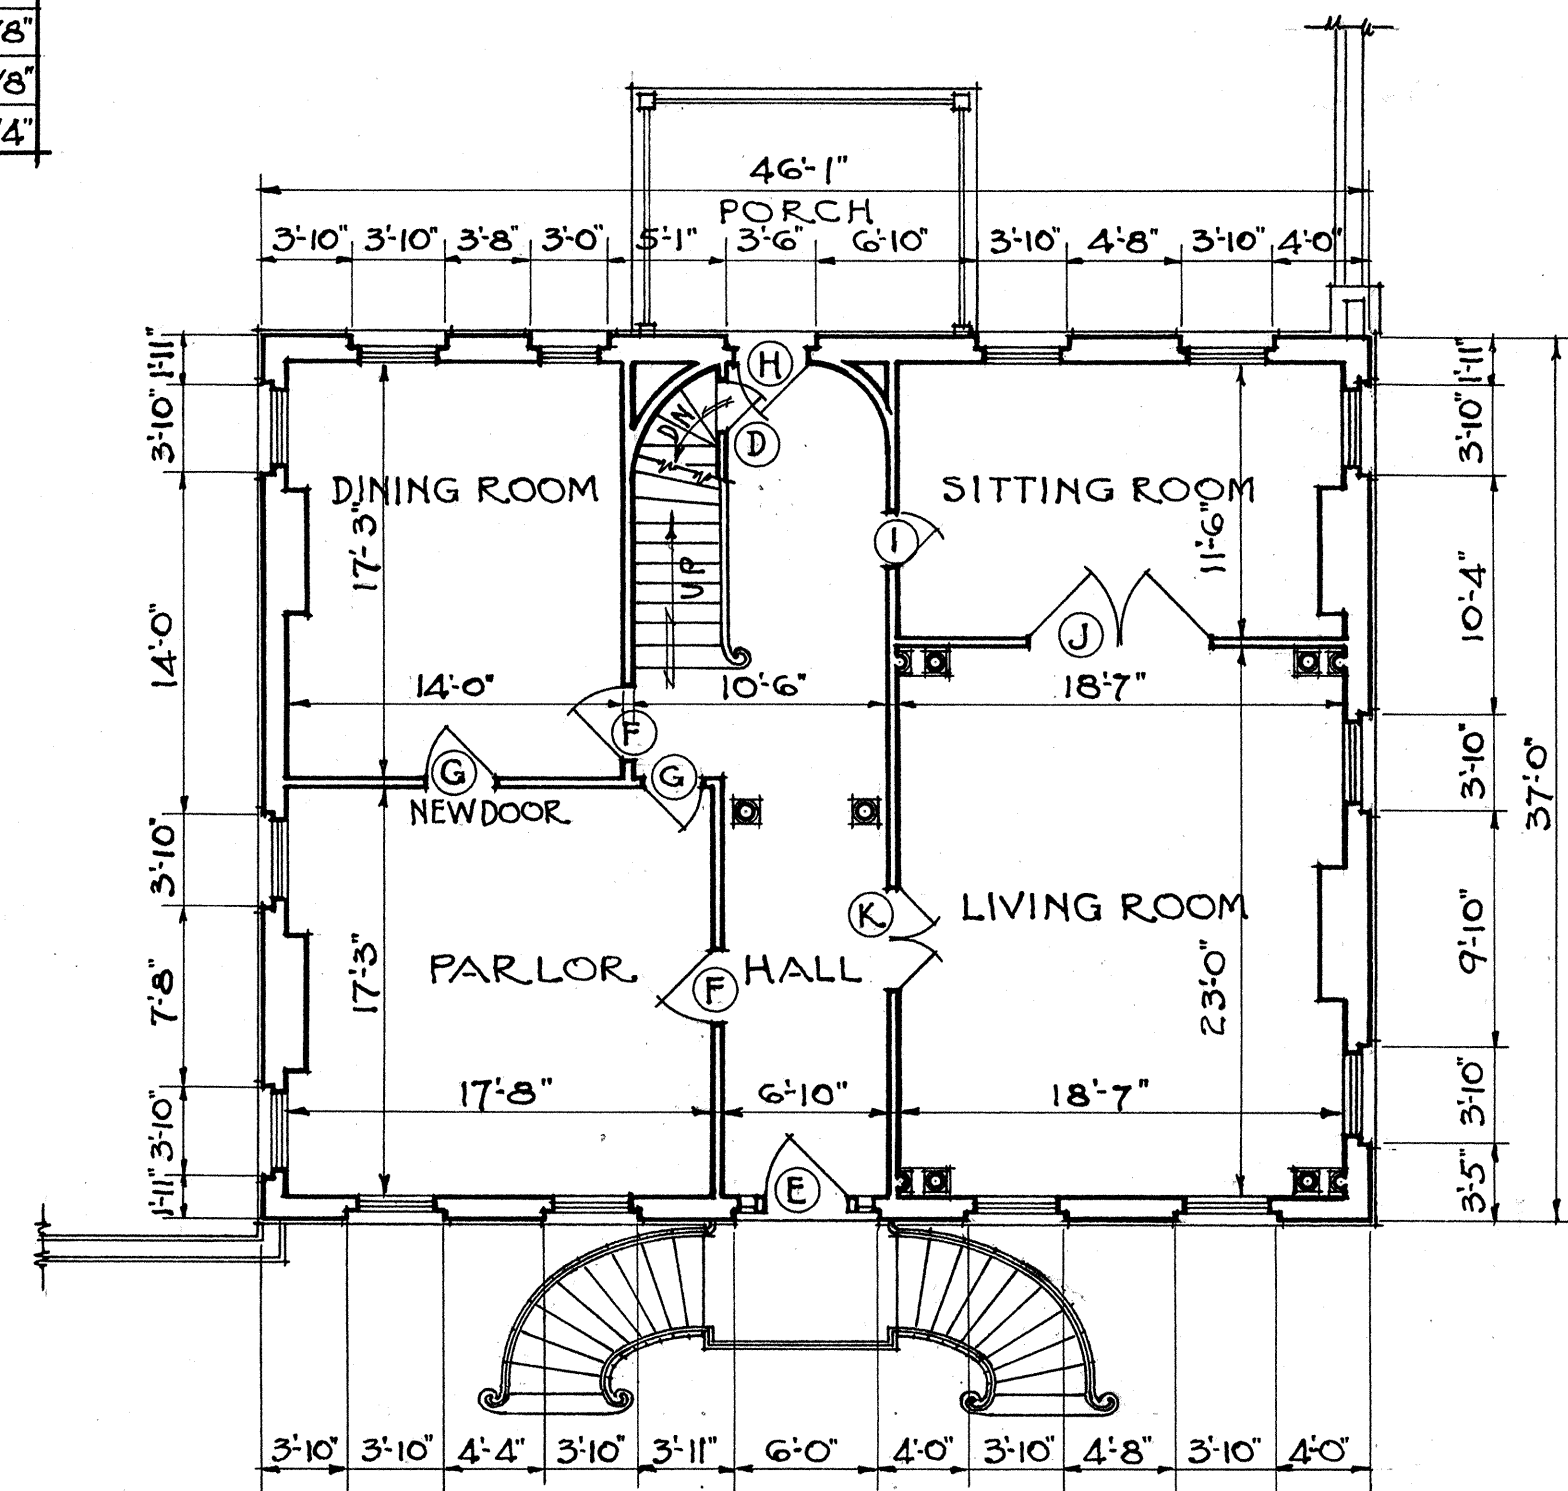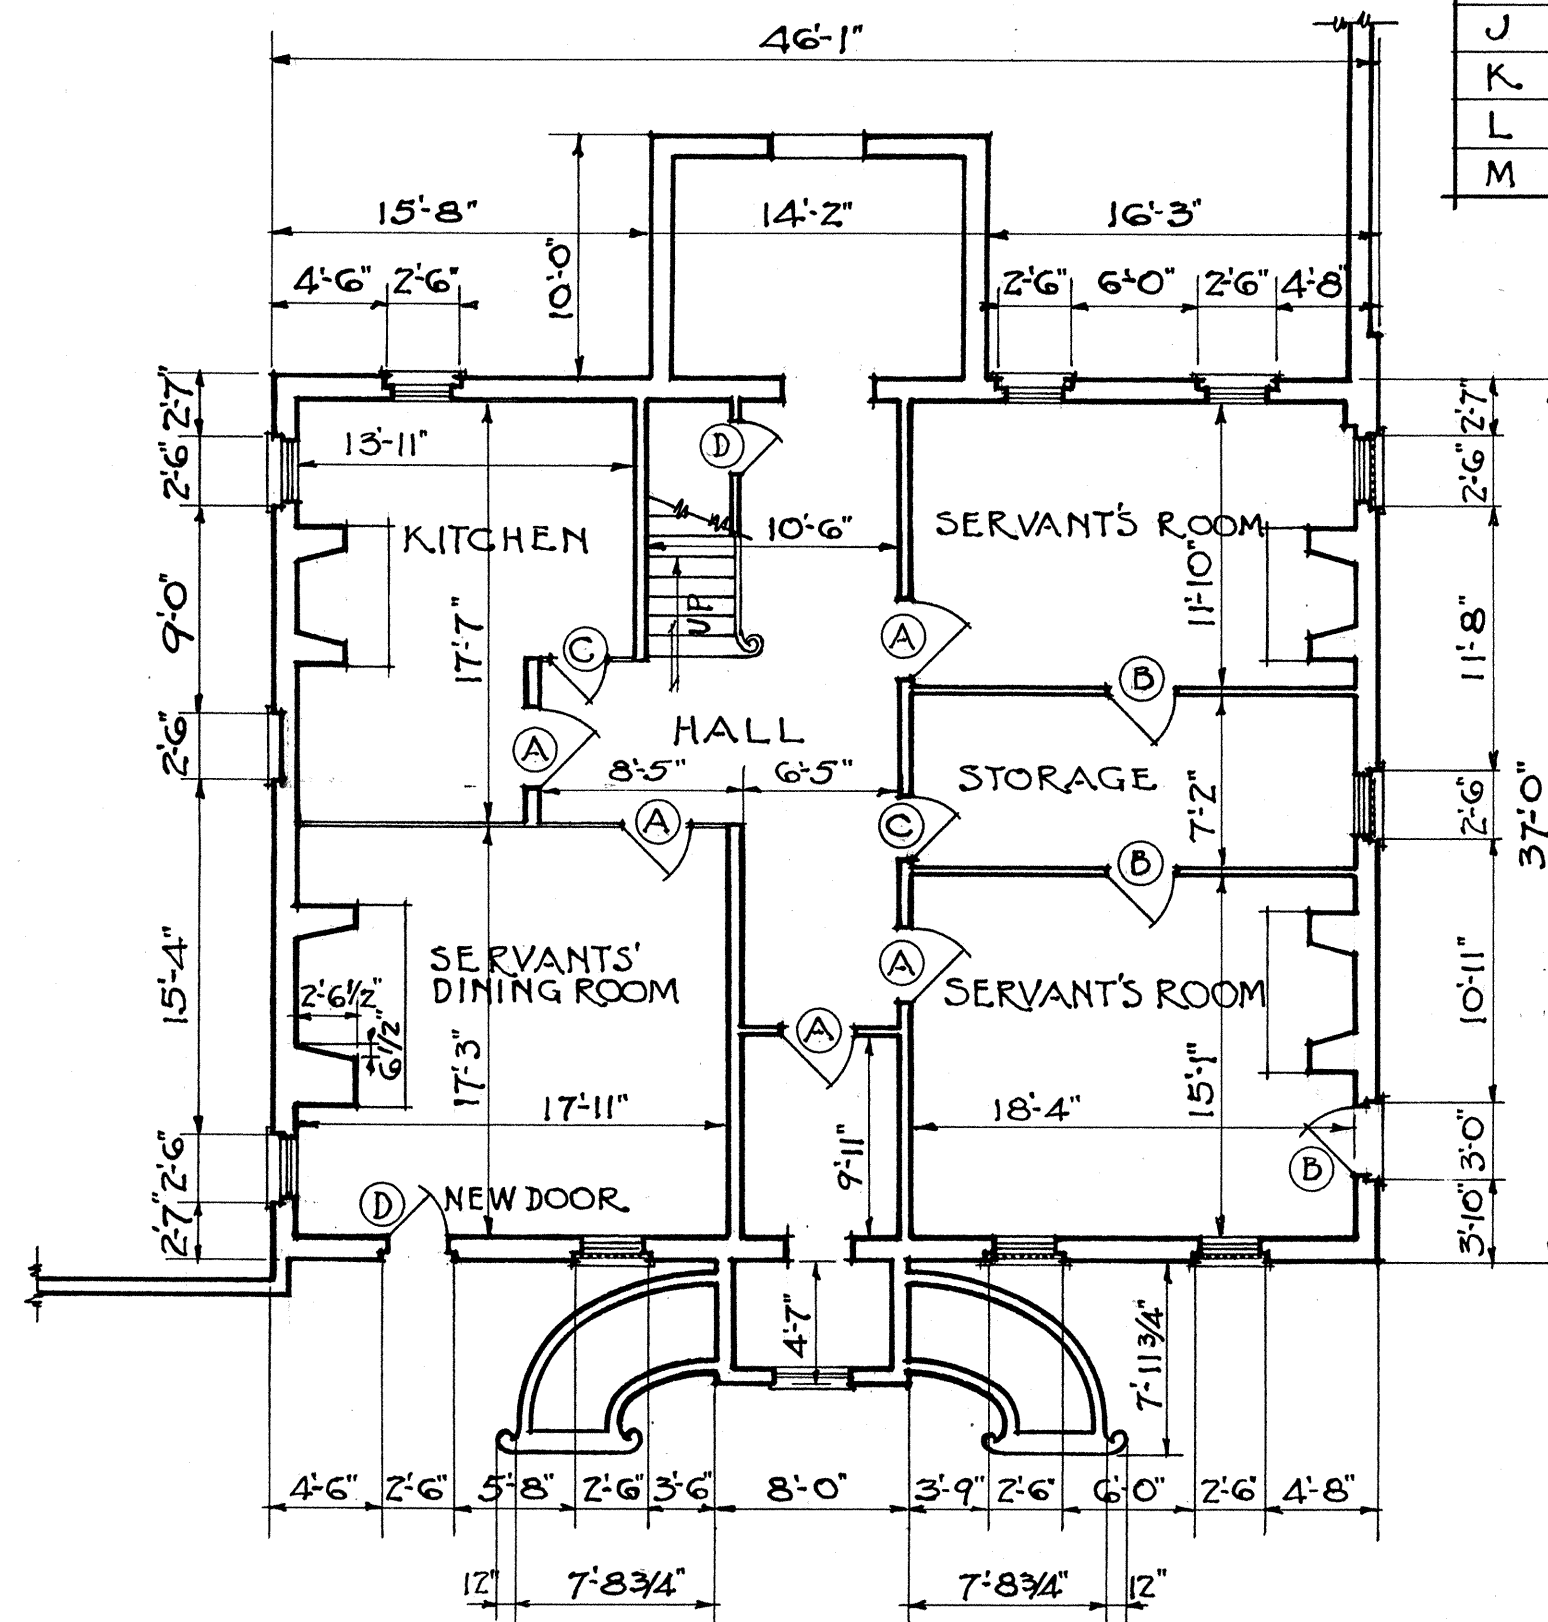

J.M. RUSSELL DEL.

U.S. DEPARTMENT OF THE INTERIOR
OFFICE OF NATIONAL PARKS, BUILDINGS, AND RESERVATIONS
BRANCH OF PLANS AND DESIGN

DAVENPORT HOUSE

NAME OF STRUCTURE

SAVANNAH
CHATHAM COUNTY GEORGIA

SURVEY NO.
14-8

HISTORIC AMERICAN
BUILDINGS SURVEY
SHEET 1 OF 5 SHEETS

INDEX NO.
GA.
26-SAV
6